



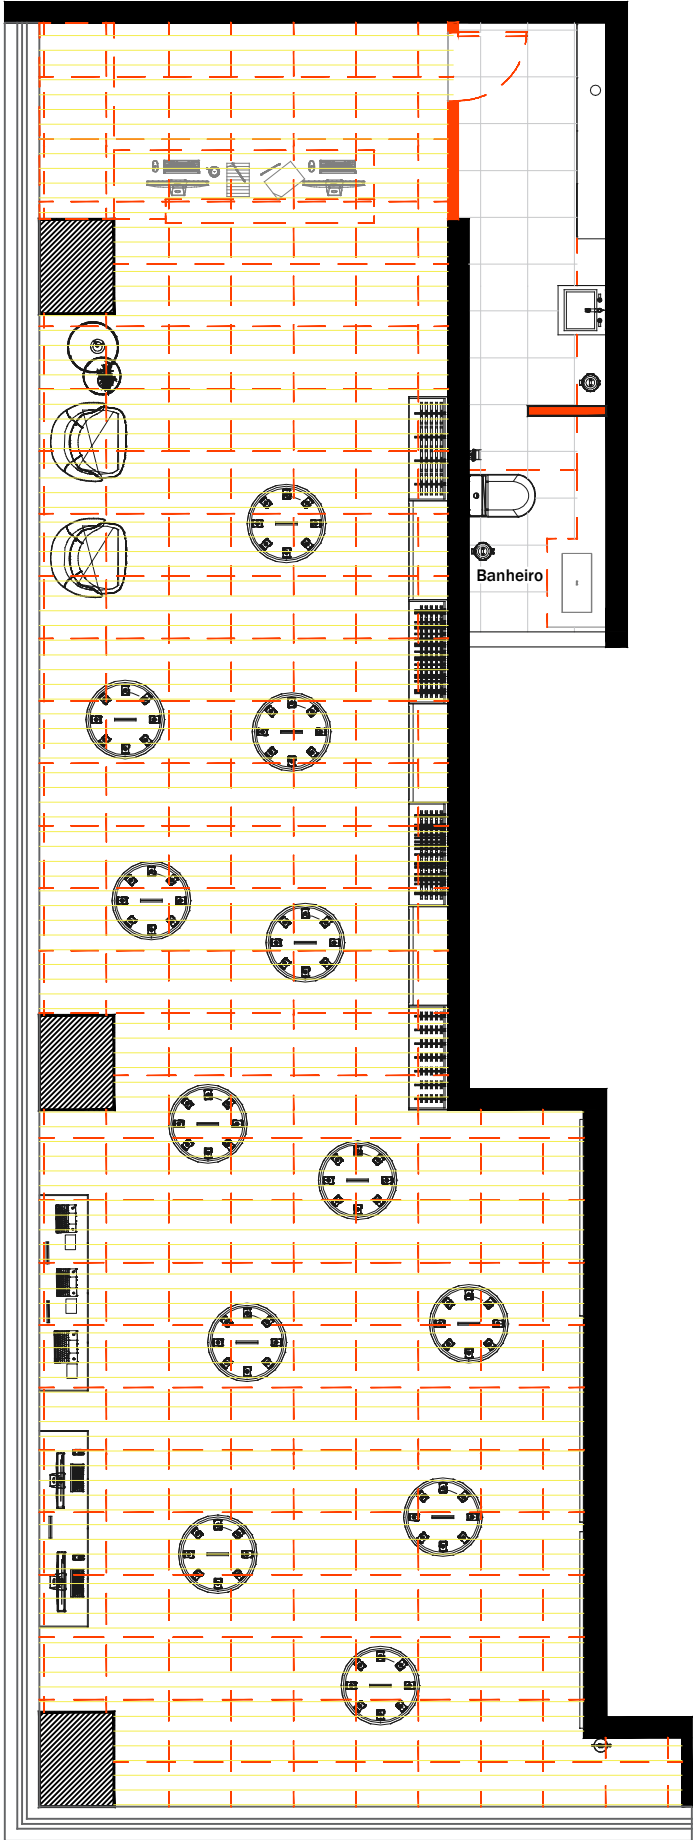

LEGENDA


- Existente e a Manter
- A Demolir
- A Construir

PLANTA BAIXA - Vermelhos e Amarelos

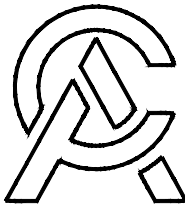

AGO - EAC

-	24 FEVER 26	V3
NO:	DATA:	DESCRIÇÃO:
PROJETO ELABORADO POR: ARQ. JONILSON CAGIZA		
DESENHOU: ARQ. JONILSON CAGIZA		
VERIFICOU: ARQ. BELARMINO MORAIS		
"CADA PROJETO É UMA OBRA PRIMA" EAC_ARQUITETURA		
PROPRIETÁRIO: BAOBABAY		
TÍTULO DO PROJETO: PROJETO COMERCIAL		
FASE DO PROJETO: LICENCIAMENTO		
LOCALIZAÇÃO DO PROJETO: BAIRRO TALATONA, MUNICÍPIO DE BELAS, PROVÍNCIA LUANDA		
TÍTULO DA FOLHA: PLANTA BAIXA VERMELHO E AMARELOS		
PROJETO Nº EAC-1903-26		
ESCALA: 1/100	FOLHA Nº	
A3	01	

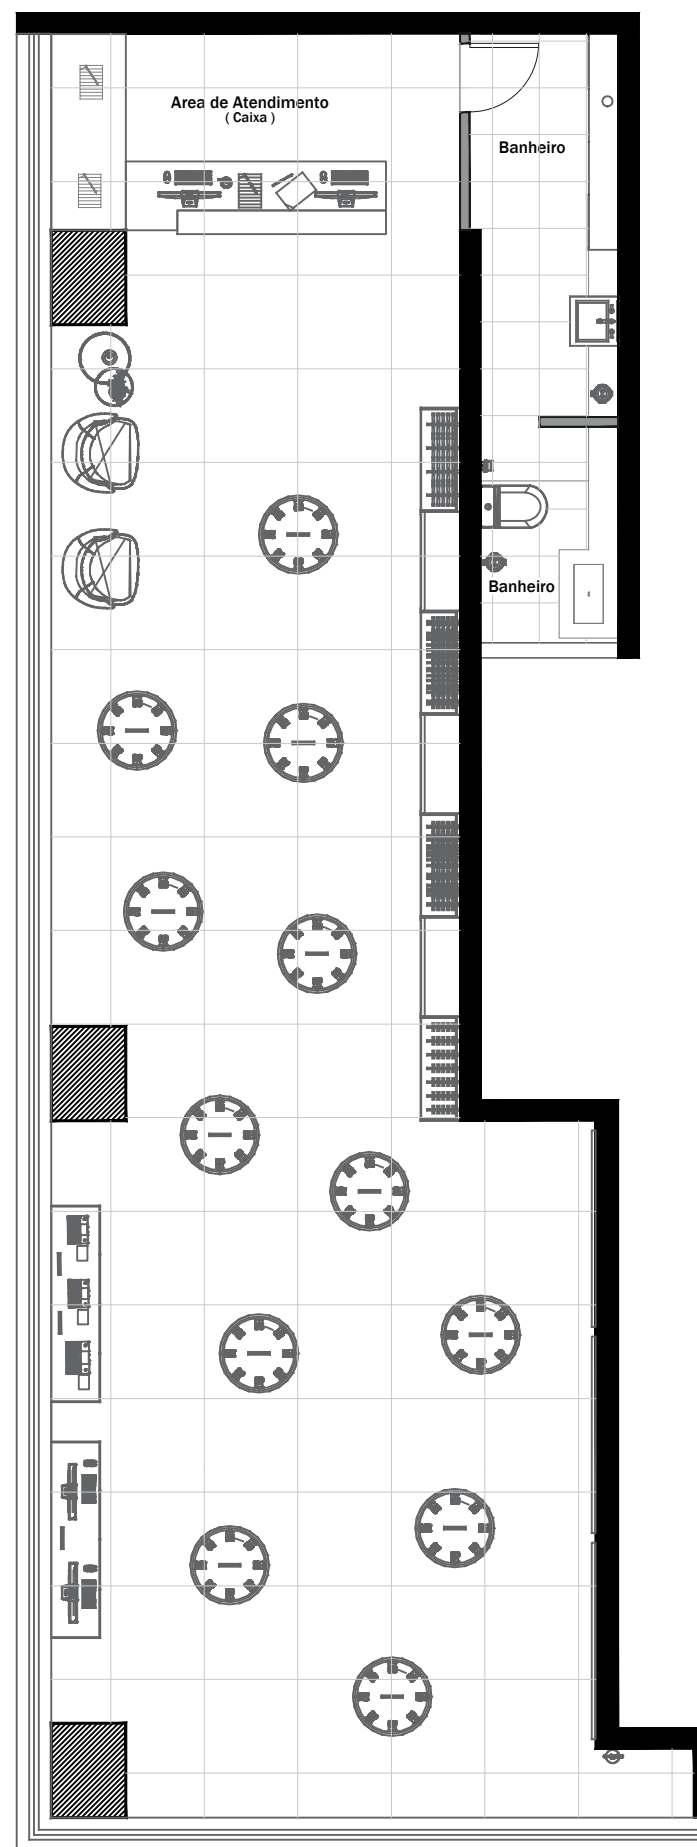

PLANTA GERAL

LEGENDA: DESCRIÇÃO / SERVIÇOS


- 01 ESCOMBRO COMPACTADO
- 02 REGULARIZAÇÃO DO CONTRAPISO
- 03 PISO EM PORCELANATO LIMESTONE WHITE 60x60cm
- 04 LAJE DE PAVIMENTO EM BETÃO ARMADO
- 05 TECTO FALSO EM FORRO DE GESSO CARTONADO FIXADO COM TABIQUES E ACABAMENTO, ESTUQUE E PINTURA
- 06 PORTA EM CONTRAPLACADO LACADO DE COR BRANCO H=2.10 m – PORTAS PIVOTANTES
- 07 ESPELHO 0.50x0.85Cm
- 08 PINTURA NEUSE / CIN COR BRANCO SOBRE MASSA CORRIDA PVA (OU SIMILAR)

LEGENDA:

- PAREDE EM ALVENARIA
- CERAMICOS


ALVENARIAS

- PAREDE EM ALVENARIA
- PISO EM PORCELANATO LIMESTONE WHITE 60X60 – PISO 0

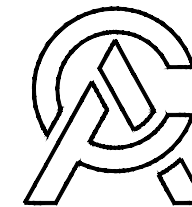

AGO - EAC


-	24 FEVER 26	V3
NO:	DATA:	DESCRIÇÃO:
PROJETO ELABORADO POR: ARQ. JONILSON CAGIZA		
DESENHOU: ARQ. JONILSON CAGIZA		
VERIFICOU: ARQ. BELARMINO MORAIS		
"CADA PROJETO É UMA OBRA PRIMA" EAC_ARQUITETURA		
PROPRIETÁRIO: BAOBABAY		
TÍTULO DO PROJETO: PROJETO COMERCIAL		
FASE DO PROJETO: LICENCIAMENTO		
LOCALIZAÇÃO DO PROJETO: BAIRRO TALATONA, MUNICÍPIO DE BELAS, PROVÍNCIA LUANDA		
TÍTULO DA FOLHA: PLANTA GERAL		
PROJETO Nº EAC-1903-26		
ESCALA: 1/100	FOLHA Nº 02	
A3		

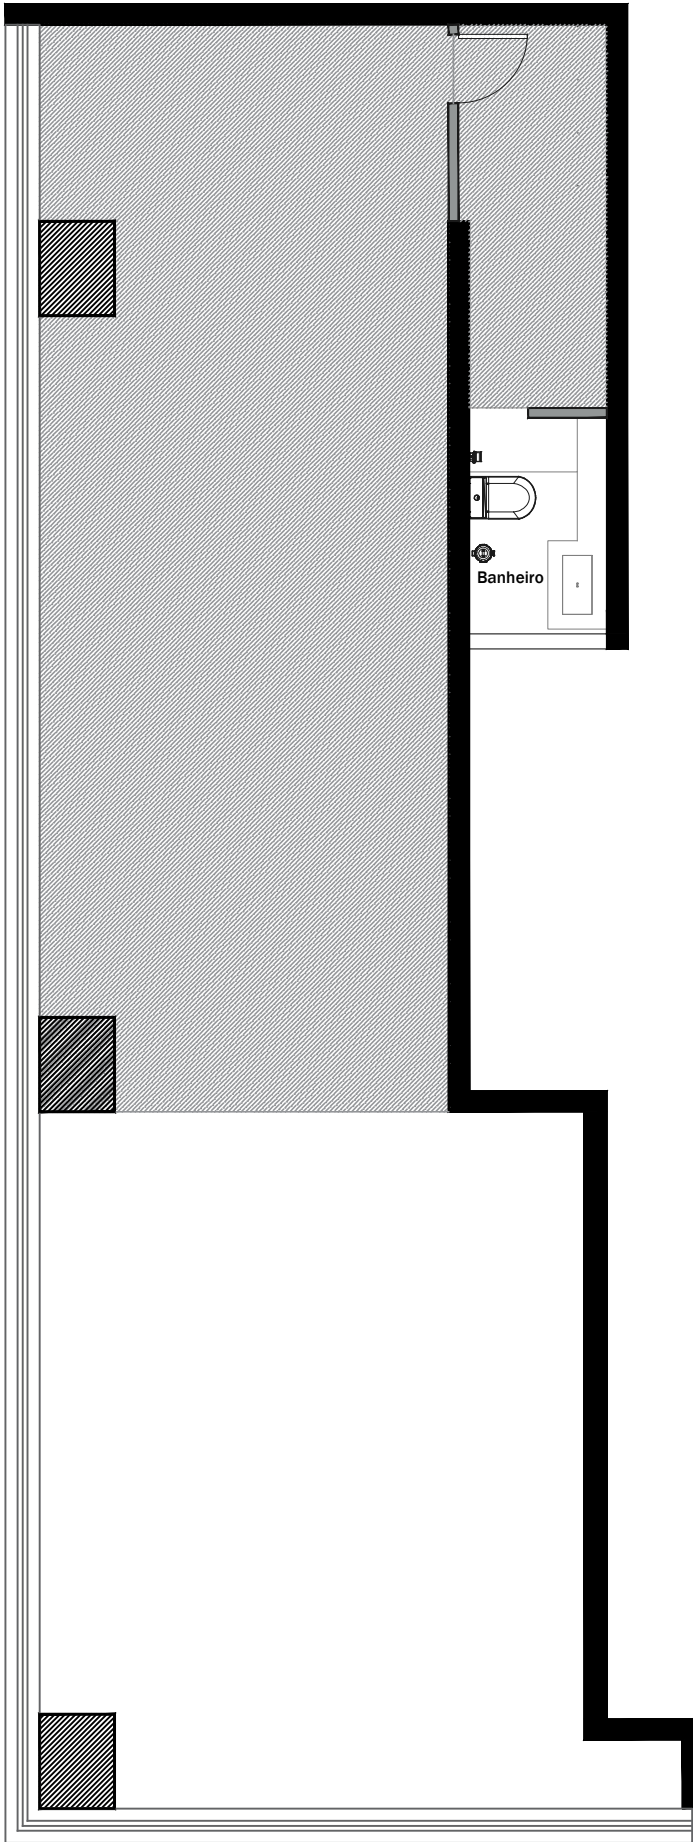

PLANTA BAIXA - Teto

LEGENDA

— Teto falso em gesso
acartonado

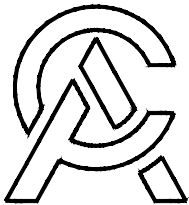


AGO - EAC


-	24 FEVER 26	V3
NO:	DATA:	DESCRIÇÃO:
PROJETO ELABORADO POR: ARQ. JONILSON CAGIZA		
DESENHOU: ARQ. JONILSON CAGIZA		
VERIFICOU: ARQ. BELARMINO MORAIS		
"CADA PROJETO É UMA OBRA PRIMA" EAC_ARQUITETURA		
PROPRIETÁRIO: BAOBABAY		
TÍTULO DO PROJETO: PROJETO COMERCIAL		
FASE DO PROJETO: LICENCIAMENTO		
LOCALIZAÇÃO DO PROJETO: BAIRRO TALATONA, MUNICÍPIO DE BELAS, PROVÍNCIA LUANDA		
TÍTULO DA FOLHA: IMAGEM DE CONSEITO		
PROJETO Nº EAC-1903-26		
ESCALA: 1/100	FOLHA Nº 03	
A3		




1 IMAGEM RENDERIZADA
ESCALA: 1/100
OBS.: CONFERIR COTAS NA OBRA

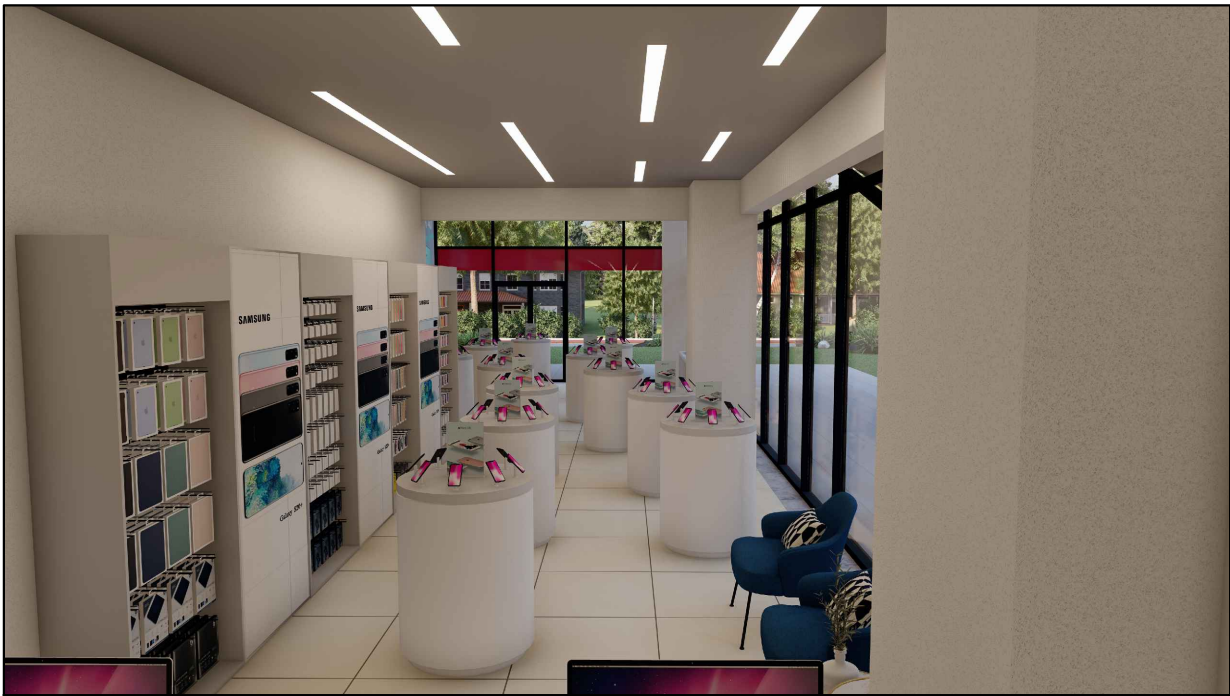


2 IMAGEM RENDERIZADA
ESCALA: 1/100
OBS.: CONFERIR COTAS NA OBRA

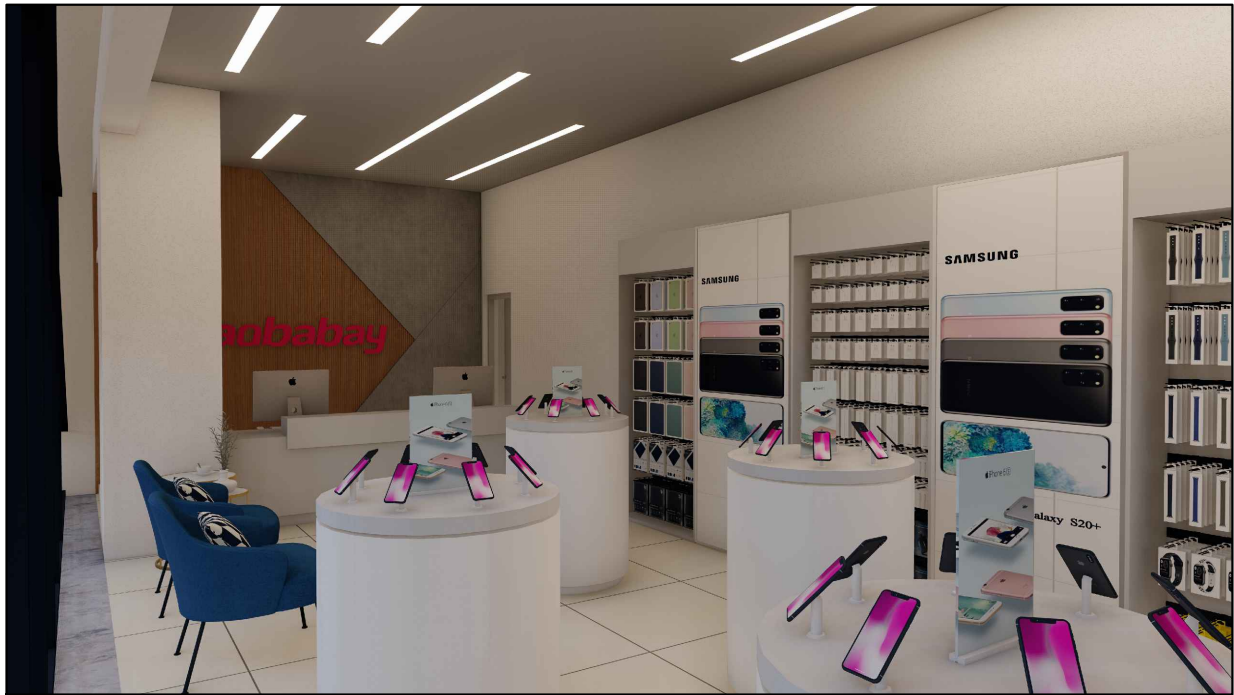

3 IMAGEM RENDERIZADA
ESCALA: 1/100
OBS.: CONFERIR COTAS NA OBRA

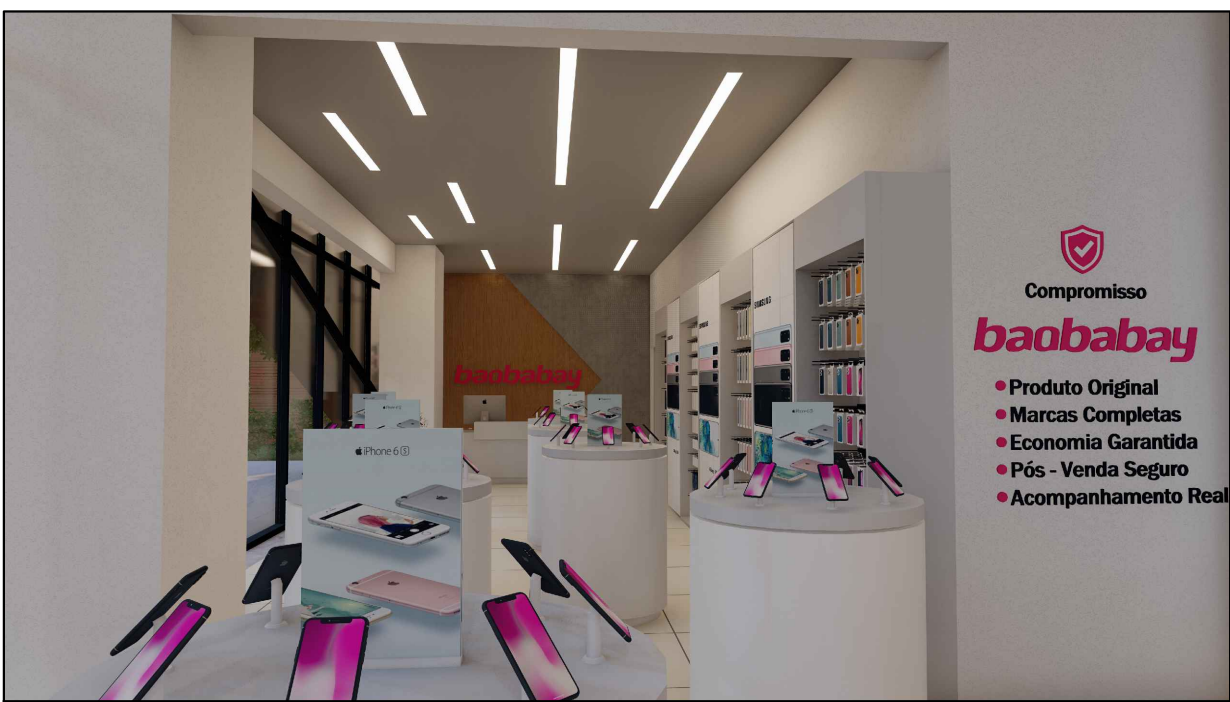

4 IMAGEM RENDERIZADA
ESCALA: 1/100
OBS.: CONFERIR COTAS NA OBRA

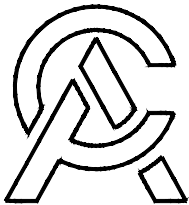

AGO - EAC

-	24 FEVER 26	V3
---	-------------	----

NO:	DATA:	DESCRIÇÃO:
-----	-------	------------

PROJETO ELABORADO POR:
ARQ. JONILSON CAGIZA

DESENHOU:
ARQ. JONILSON CAGIZA

VERIFICOU:
ARQ. BELARMINO MORAIS

"CADA PROJETO É UMA OBRA PRIMA"
EAC_ARQUITETURA

PROPRIETÁRIO:
BAOBABAY

TÍTULO DO PROJETO:
PROJETO COMERCIAL

FASE DO PROJETO:
PROJETO LEGAL

LOCALIZAÇÃO DO PROJETO:
BAIRRO TALATONA, MUNICÍPIO DE
BELAS, PROVÍNCIA LUANDA

TÍTULO DA FOLHA:
IMAGEM DE CONSEITO

PROJETO Nº
EAC-1903-26

ESCALA: 1/100	FOLHA Nº 04
------------------	----------------