


AGO - EAC


NO:	DATA:	DESCRIÇÃO:
PROJETO ELABORADO POR: ARQ.JONILSON CAGIZA		
DESENHOU: ARQ.JONILSON CAGIZA		
VERIFICOU: ARQ.BELARMINO MORAIS		
"CADA PROJETO É UMA OBRA PRIMA" EAC_ARQUITETURA		
PROPRIETÁRIO: BAOBABAY		
TÍTULO DO PROJETO: PROJETO DE REFORMA		
FASE DO PROJETO: PROJ. LICENCIAMENTO		
LOCALIZAÇÃO DO PROJETO: BAIRRO CAMAMA, PROVÍNCIA LUANDA - ANGOLA		
DESCRIÇÃO: PLANTA BAIXA DE VERMELHO E AMARELO		
ESPECIALIDADE: ARQUITETURA		
PROJETO Nº EAC-1803-26		
ESCALA: 1/100	FOLHA Nº	
A3	01	

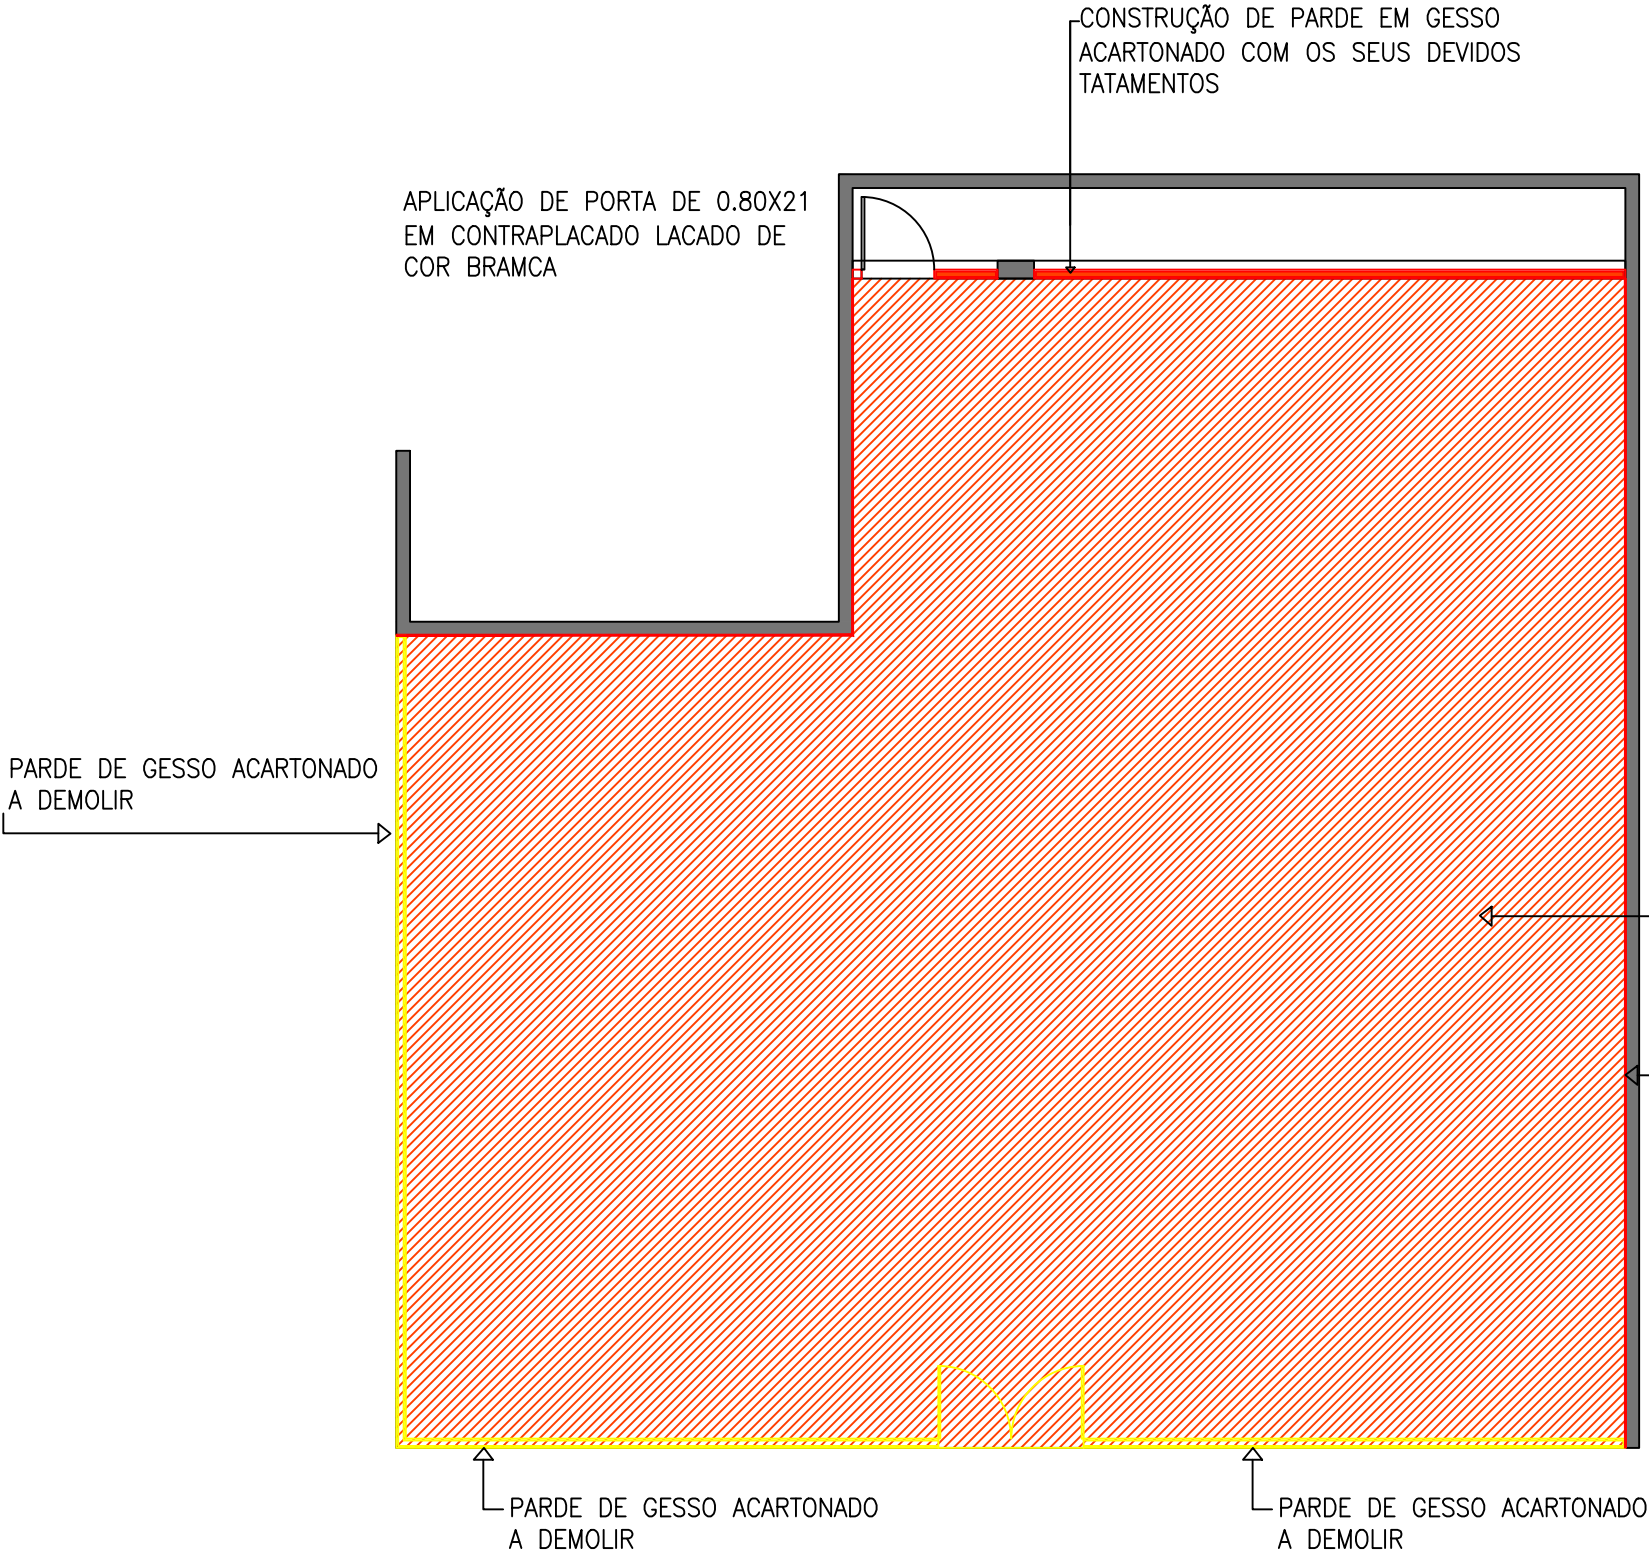

1 PLANTA BAIXA DE VERMELHO E AMARELO

ESCALA: 1/100

OBS.: CONFERIR COTAS NA OBRA

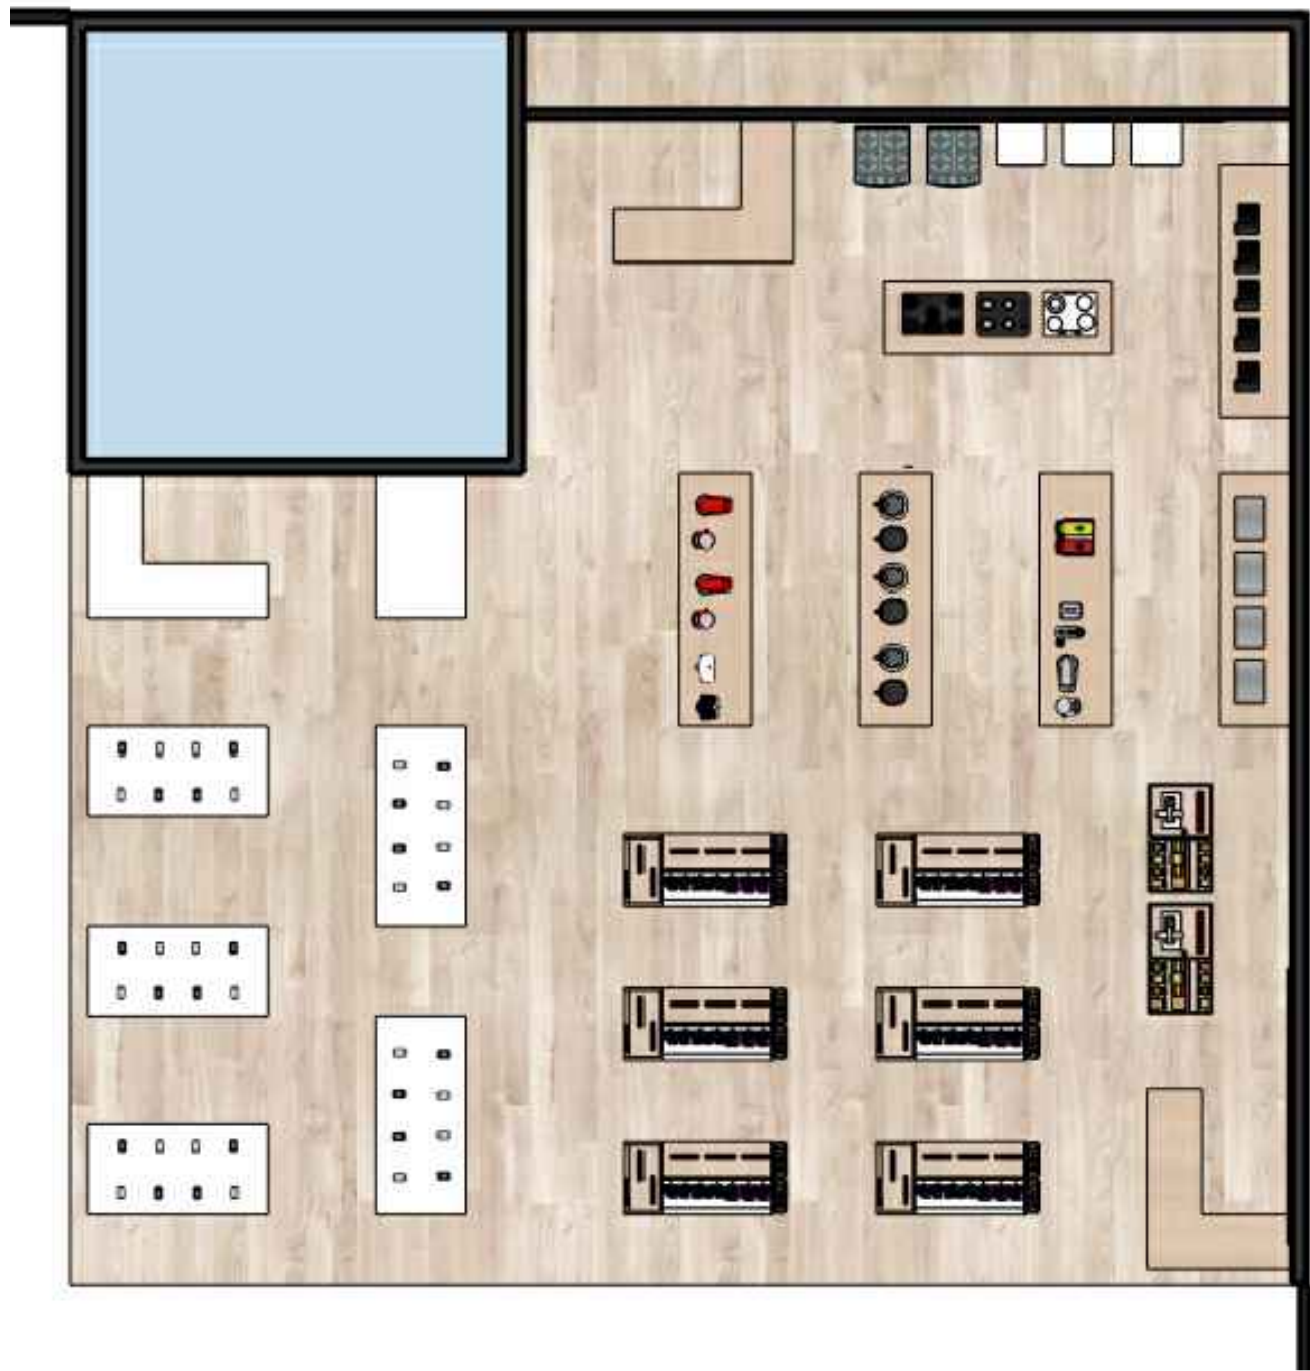

1 PLANTA BAIXA GERAL
ESCALA: 1/100
OBS.: CONFERIR COTAS NA OBRA

LEGENDA: DESCRIÇÃO / SERVIÇOS


- 01 REGULARIZAÇÃO DO CONTRAPISO
- 02 PISO EM PORCELANATO LIMESTONE WHITE 60x60cm
- 03 LAJE DE PAVIMENTO EM BETÃO ARMADO
- 04 TECTO FALSO EM FORRO DE GESSO CARTONADO FIXADO COM TABIQUES E ACABAMENTO, ESTUQUE E PINTURA
- 05 PORTA EM CONTRAPLACADO LACADO DE COR BRANCO H=2.10 m – PORTAS PIVOTANTES
- 06 PINTURA NEUSE / CIN COR BRANCO SOBRE MASSA CORRIDA PVA (OU SIMILAR)

LEGENDA:

- PAREDE EM ALVENARIA
- CERAMICOS

ALVENARIAS

- PAREDE EM ALVENARIA
- PISO EM PORCELANATO LIMESTONE WHITE 60X60 – PISO O

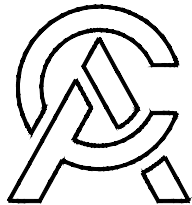

AGO - EAC

NO:	DATA:	DESCRIÇÃO:
PROJETO ELABORADO POR: ARQ.JONILSON CAGIZA		
DESENHOU: ARQ.JONILSON CAGIZA		
VERIFICOU: ARQ.BELARMINO MORAIS		
"CADA PROJETO É UMA OBRA PRIMA" EAC_ARQUITETURA		
PROPRIETÁRIO: BAOBABAY		
TÍTULO DO PROJETO: PROJETO DE REFORMA		
FASE DO PROJETO: PROJ. LICENCIAMENTO		
LOCALIZAÇÃO DO PROJETO: BAIRRO CAMAMA, PROVÍNCIA LUANDA - ANGOLA		
DESCRIÇÃO: PLANTA BAIXA GERAL		
ESPECIALIDADE: ARQUITETURA		
PROJETO Nº EAC-1803-26		
ESCALA: 1/100	FOLHA Nº	
A3	02	



1 IMAGEM RENDERIZADA
ESCALA: 1/100
OBS.: CONFERIR COTAS NA OBRA




2 IMAGEM RENDERIZADA
ESCALA: 1/100
OBS.: CONFERIR COTAS NA OBRA



3 IMAGEM RENDERIZADA
ESCALA: 1/100
OBS.: CONFERIR COTAS NA OBRA



4 IMAGEM RENDERIZADA
ESCALA: 1/100
OBS.: CONFERIR COTAS NA OBRA

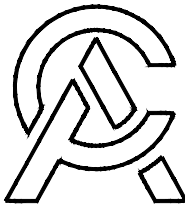

AGO - EAC

NO: DATA: DESCRIÇÃO:

PROJETO ELABORADO POR:
ARQ.JONILSON CAGIZA

DESENHOU:
ARQ.JONILSON CAGIZA

VERIFICOU:
ARQ.BELARMINO MORAIS

"CADA PROJETO É UMA OBRA PRIMA"
EAC_ARQUITETURA

PROPRIETÁRIO:
BAOBABAY

TÍTULO DO PROJETO:
PROJETO DE REFORMA

FASE DO PROJETO:
PROJ. LICENCIAMENTO

LOCALIZAÇÃO DO PROJETO:
BAIRRO CAMAMA, PROVÍNCIA LUANDA -
ANGOLA

DESCRIÇÃO:
IMAGENS RENDERIZADAS

ESPECIALIDADE:
ARQUITETURA


PROJETO Nº
EAC-1803-26

ESCALA:
1/100


FOLHA Nº

A3

03

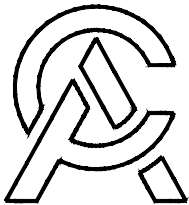


AGO - EAC

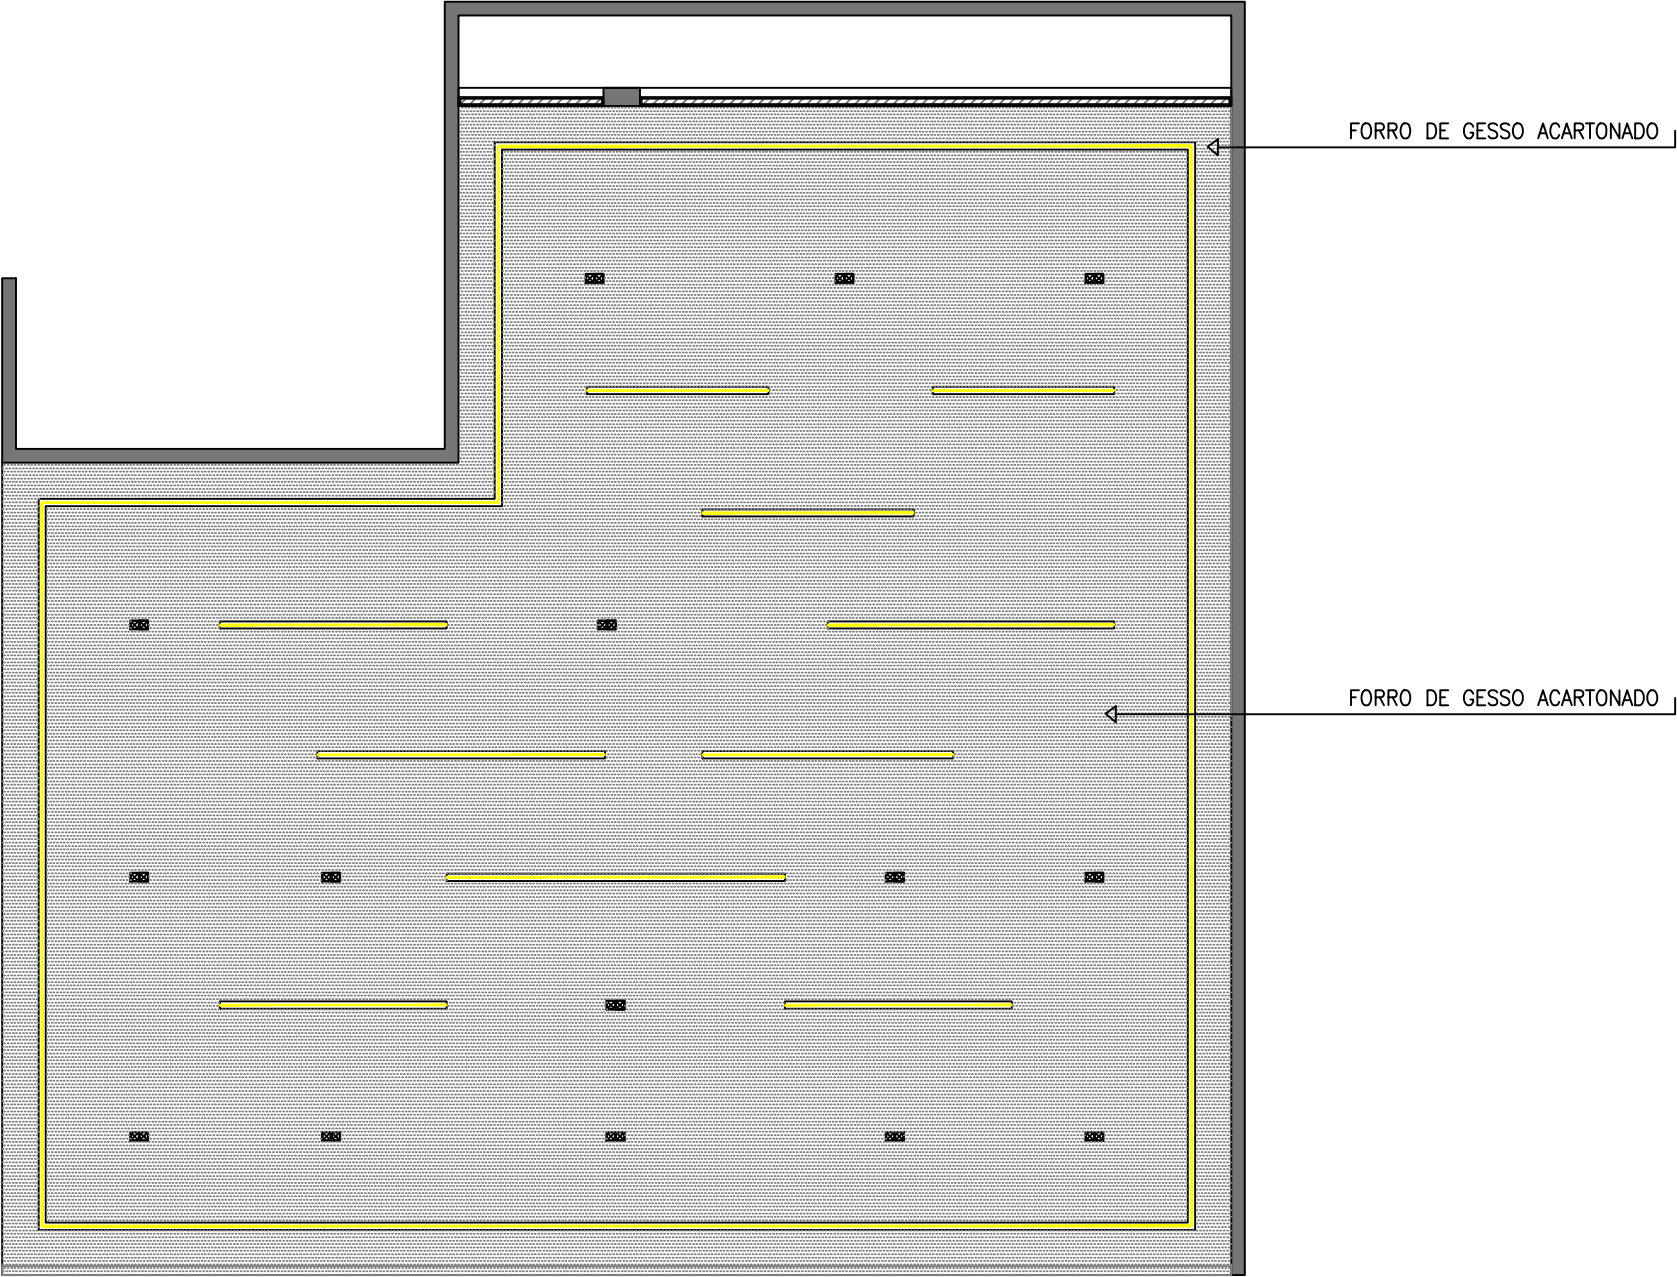

1 PLANTA DE FORRO DE GESSO
ESCALA: 1/100
OBS.: CONFERIR COTAS NA OBRA


NO:	DATA:	DESCRIÇÃO:
PROJETO ELABORADO POR: ARQ.JONILSON CAGIZA		
DESENHOU: ARQ.JONILSON CAGIZA		
VERIFICOU: ARQ.BELARMINO MORAIS		
"CADA PROJETO É UMA OBRA PRIMA" EAC_ARQUITETURA		
PROPRIETÁRIO: BAOBABAY		
TÍTULO DO PROJETO: PROJETO DE REFORMA		
FASE DO PROJETO: PROJ. LICENCIAMENTO		
LOCALIZAÇÃO DO PROJETO: BAIRRO CAMAMA, PROVÍNCIA LUANDA - ANGOLA		
DESCRIÇÃO: PLANTA BAIXA DE FORRO DE GESSO		
ESPECIALIDADE: ARQUITETURA		
PROJETO Nº EAC-1803-26		
ESCALA: 1/100	FOLHA Nº	
A3	04	

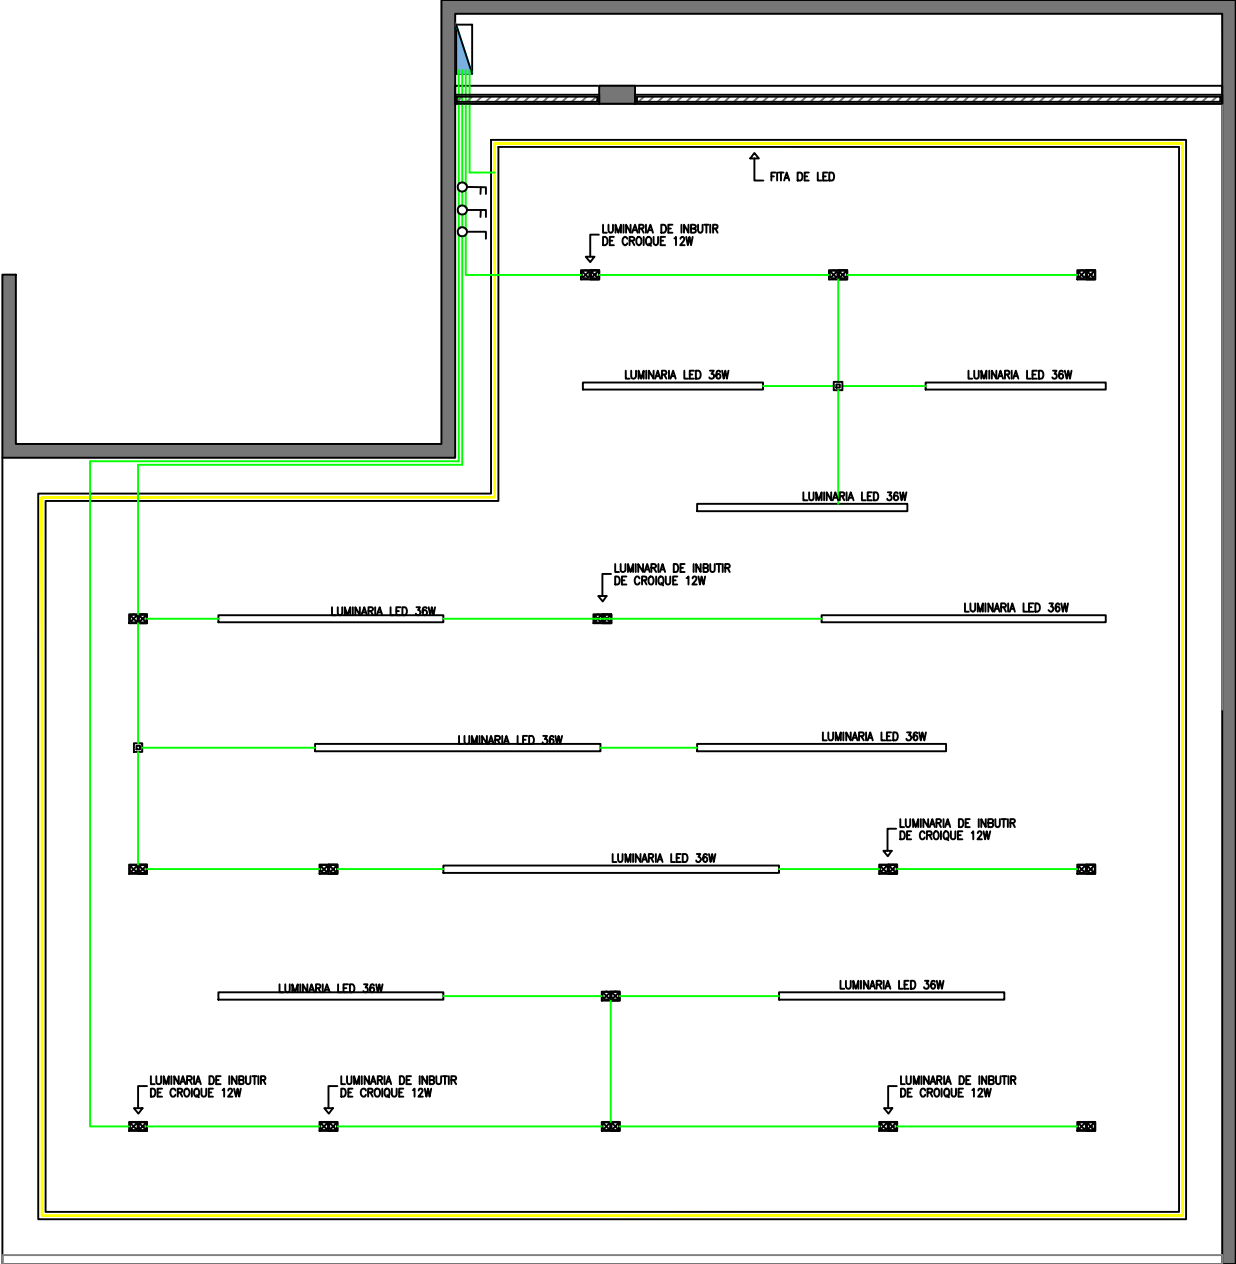

LEGENDA DE SIMBOLOS


SIMBOLO	DESIGNAÇÃO
	LUMINARIA LED 36W
	LUMINARIA LED 12W EMBUTIDA NO TECTO FALSO
	INTERRUPTOR DUPLO
	INTERRUPTOR SIMPLES
	QUADRO ELÉTRICO
	CAIXA DE PASSAGEM ACIMA DO TECTO FALSO

1 PLANTA BAIXA DE ILUMINAÇÃO
ESCALA: 1/100
OBS.: CONFERIR COTAS NA OBRA

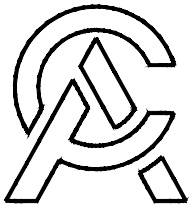


AGO - EAC

	DATA:	DESCRIÇÃO:
PROJETO ELABORADO POR: ARQ.JONILSON CAGIZA		
DESENHOU: ARQ.JONILSON CAGIZA		
VERIFICOU: ARQ.BELARMINO MORAIS		
"CADA PROJETO É UMA OBRA PRIMA" EAC_ARQUITETURA		
PROPRIETÁRIO: BAOBABAY		
TÍTULO DO PROJETO: PROJETO DE REFORMA		
FASE DO PROJETO: PROJ. LICENCIAMENTO		
LOCALIZAÇÃO DO PROJETO: BAIRRO CAMAMA, PROVÍNCIA LUANDA - ANGOLA		
DESCRIÇÃO: PLANTA DE ILUMINAÇÃO		
ESPECIALIDADE: PROJETO ELÉTRICO		
PROJETO Nº EAC-1803-26		
ESCALA: 1/100	FOLHA Nº 05	
A3		

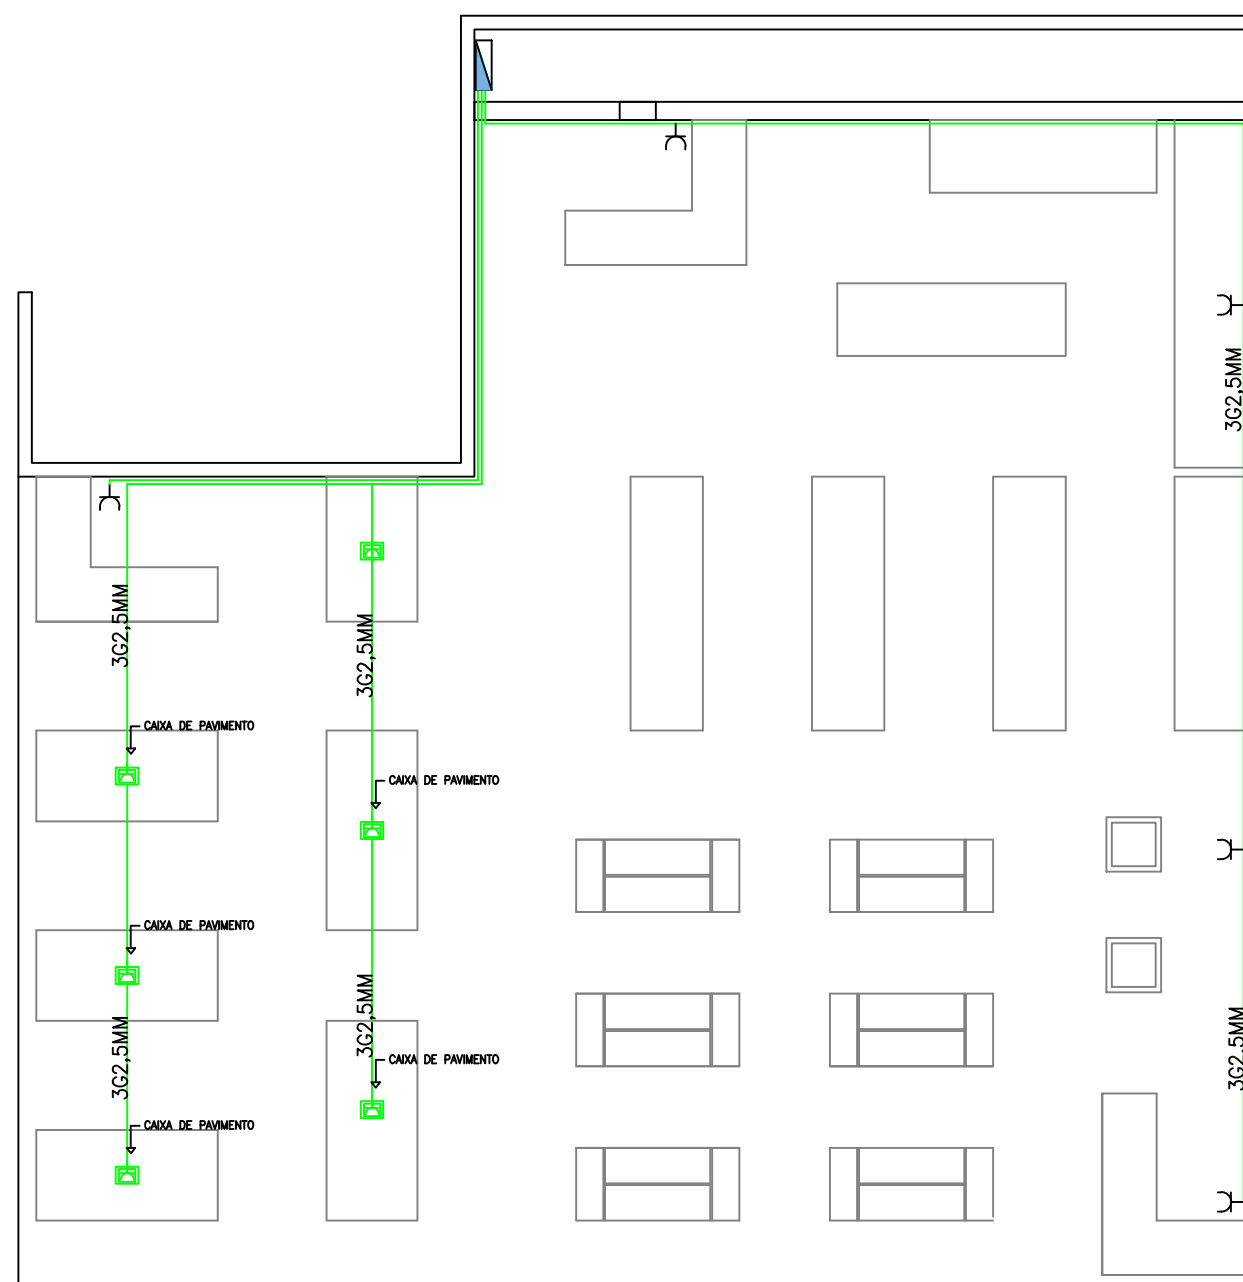


LEGENDA DE SIMBOLOS

SÍMBOLO	DESIGNAÇÃO
	QUADRO ELÉTRICO
	TOMADA TRIFÁSICA COM LIGALÃO A TERRA CAIXA DE PAVIMENTO MAIS TOMADA
	TOMADA SIMPLES

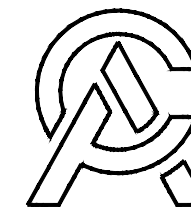

AGO - EAC

	DATA:	DESCRIÇÃO:
PROJETO ELABORADO POR: ARQ.JONILSON CAGIZA		
DESENHOU: ARQ.JONILSON CAGIZA		
VERIFICOU: ARQ.BELARMINO MORAIS		
"CADA PROJETO É UMA OBRA PRIMA" EAC_ARQUITETURA		
PROPRIETÁRIO: BAOBABAY		
TÍTULO DO PROJETO: PROJETO DE REFORMA		
FASE DO PROJETO: PROJ. LICENCIAMENTO		
LOCALIZAÇÃO DO PROJETO: BAIRRO CAMAMA, PROVÍNCIA LUANDA - ANGOLA		
DESCRIÇÃO: TOMADAS E ALIMENTAÇÃO DE EQUIPAMENTO		
ESPECIALIDADE: PROJETO ELÉTRICO		
PROJETO Nº EAC-1803-26		
ESCALA: 1/100	FOLHA Nº	
A3	06	

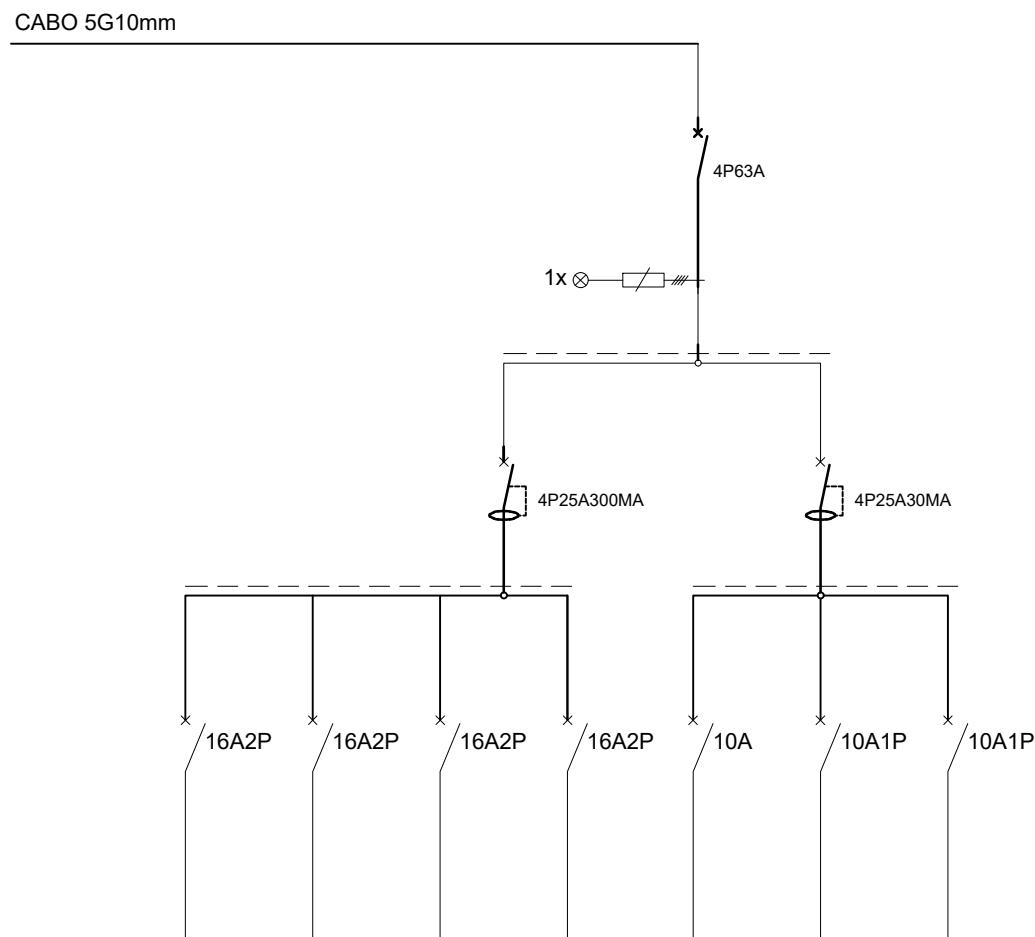

# CIRC.	IL1	IL2	IL3	IL4		T2	T3
FASE(S)	L1	L1	L1	L1	L1	L1	L1
POT.(VA)	--	--	--	--	--	--	--
CANALIZAÇÕES	H1W-U3G1,5 TUBO VD25	H1W-U3G1,5 TUBO VD25	H1W-U3G1,5 TUBO VD25	H1W-U3G1,5 TUBO VD25	H1W-U3G1,5 TUBO VD25	H1W-U3G1,5 TUBO VD25	H1W-U3G1,5 TUBO VD25
DESTINO	ILUMINAÇÃO NORMAL AUDITÓRIO	ILUMINAÇÃO NORMAL AUDITÓRIO	ILUMINAÇÃO NORMAL AUDITÓRIO	ILUMINAÇÃO NORMAL	TOMADAS DE USOS GERAIS	TOMADAS DE PAVIMENTO	TOMADAS DE PAVIMENTO

NOTAS:


1 OS SINALIZADORES QUE JÁ VEM NO PRÓPRIO INVERSOR DE FASE DEVERÃO SINALIZAR O SEGUINTE:

1. VERDE - SINALIZAR PRESENÇA DE TENSÃO FASE 1

2. LARANJA - SINALIZAR PRESENÇA DE TENSÃO FASE 2

3. VERMELHA - SINALIZAR PRESENÇA DE TENSÃO FASE 3

2 TODOS OS CABOS ELETRICOS FLEXÍVEIS DEVEM SER LIGADOS AOS RESPETIVOS DISJUNTORES.

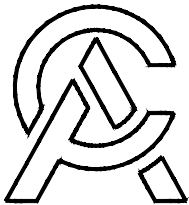

AGO - EAC

Nº:	DATA:	DESCRIÇÃO:
PROJETO ELABORADO POR: ARQ.JONILSON CAGIZA		
DESENHOU: ARQ.JONILSON CAGIZA		
VERIFICOU: ARQ.BELARMINO MORAIS		
"CADA PROJETO É UMA OBRA PRIMA" EAC_ARQUITETURA		
PROPRIETÁRIO: BAOBABAY		
TÍTULO DO PROJETO: PROJETO DE REFORMA		
FASE DO PROJETO: PROJ. LICENCIAMENTO		
LOCALIZAÇÃO DO PROJETO: BAIRRO CAMAMA, PROVÍNCIA LUANDA - ANGOLA		
DESCRIÇÃO: INSTALAÇÕES ELÉTRICAS QUADRO ELÉTRICO		
ESPECIALIDADE: PROJETO ELÉTRICO		
PROJETO Nº EAC-1803-26		
ESCALA: 1/100		FOLHA Nº
A3		07